
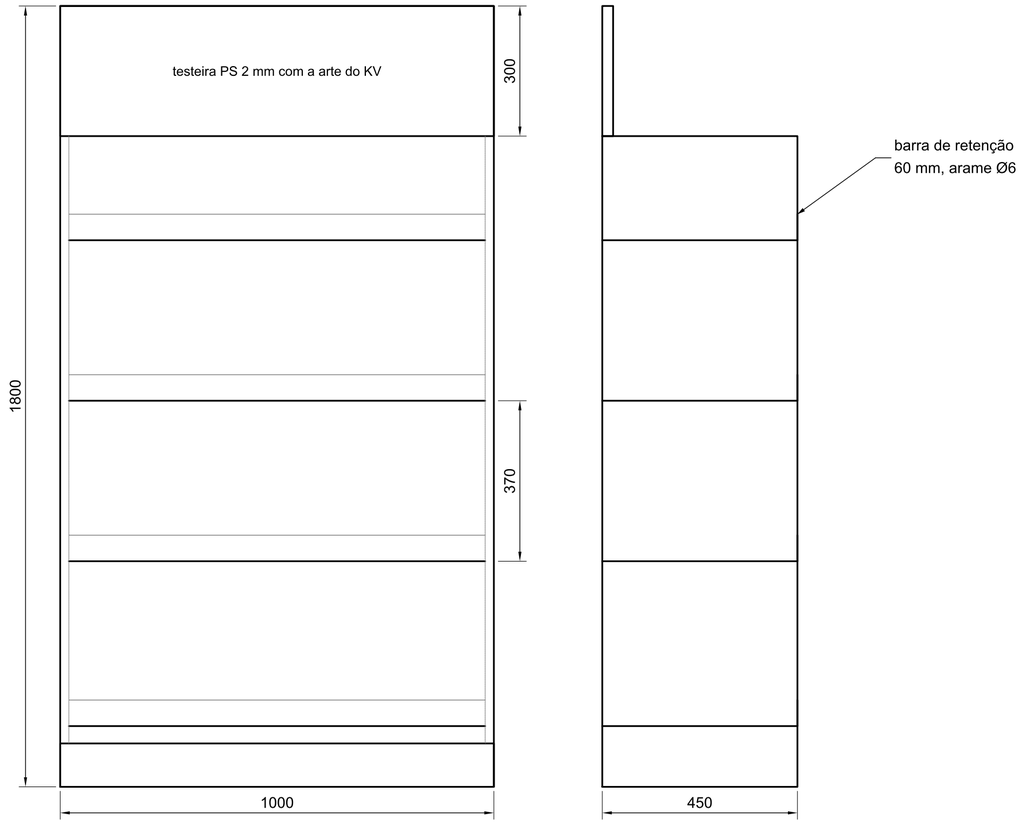


VISTA FRONTAL 1:10

VISTA LATERAL 1:10

PLANTA · GRADE 50 MM 1:10

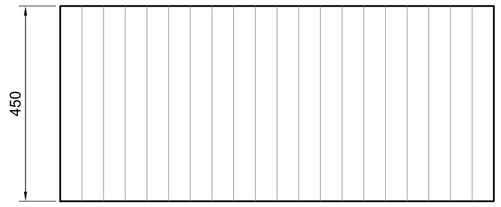

ESPECIFICAÇÃO

Estrutura: 2 laterais em tubo 20x20 mm, pintura epóxi branca.
4 prateleiras aramadas Ø4 mm, grade 50 mm, barra de retenção Ø6 a 60 mm.
Vão livre entre prateleiras 310 mm: frascos de 500 ml, 1 L e 2 L em pé.
Testeira 1000 x 300 mm em PS 2 mm impresso (arte do KV), encaixe por presilha.
Laterais em PS 2 mm 450 x 1400 mm com as flores e as cores do KV.
Rodapé em chapa 0,9 mm, 100 mm de altura, 4 sapatas niveladoras.
Capacidade: cerca de 120 frascos de 1 L (5 faixas verticais de cor).
Instalação: encostado no fim da gôndola (ponta), sem avançar no corredor.
QR único na testeira para o One Shot; tag On Timing presa no rodapé.

PERSPECTIVA ILUSTRATIVA (sem escala)



Medidas em mm pela linha de molde externa. Não medir no desenho; em caso de dúvida, valem as cotas.

75LAB projetos de PDV · 75lab.com.br	PROJETO: Escolha o perfume da sua casa · PDV		
CLIENTE: Bombril · Limpol Perfumes	MATERIAL: Aramado Ø4 mm + tubo 20x20 epóxi; PS 2 mm		
CONTEÚDO DA FOLHA: Display aramado de ponta · vistas Conjunto pesado · hiper e atacarejo			
ESCALA: 1:10	UNIDADE: mm	DATA: 20/10/2026	FOLHA: 01 / 05
REVISÃO: R00 · proposta	DESENHO: 75 LAB	FORMATO: A2 · 1º diedro	ARQUIVO: P1_display-aramado.dxf