
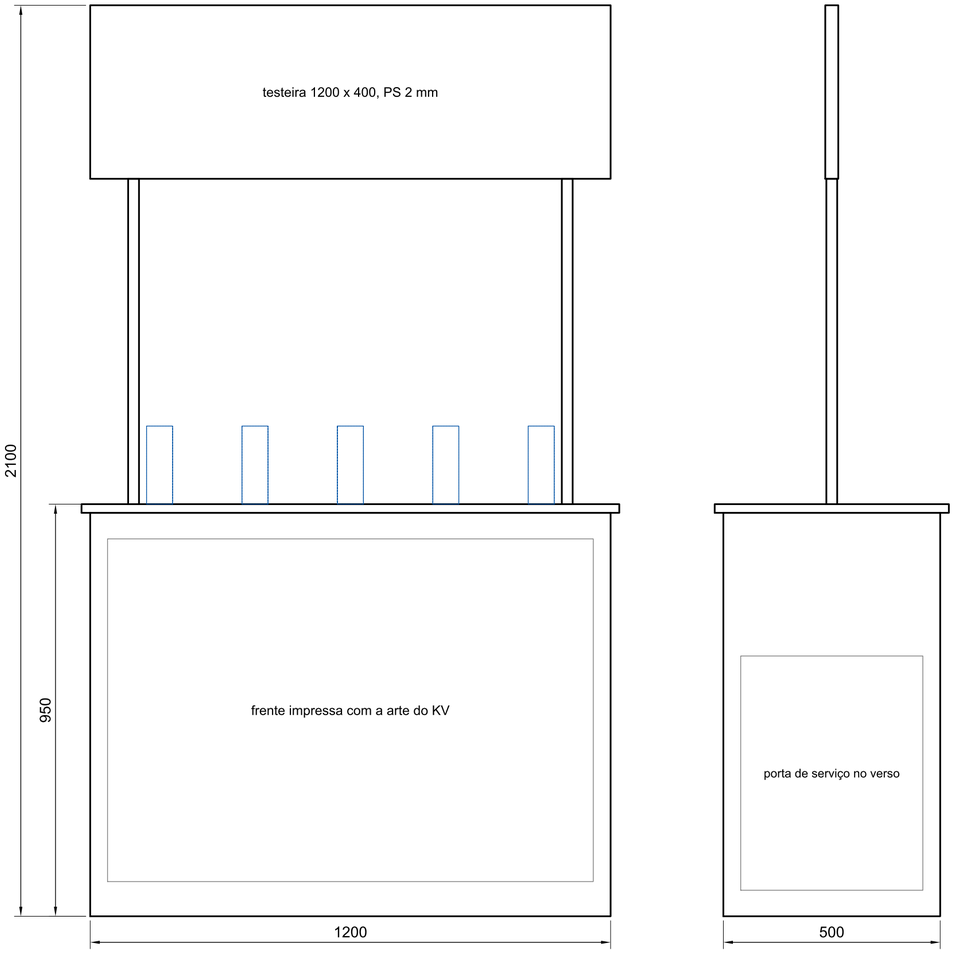


VISTA FRONTAL 1:10

VISTA LATERAL 1:10

PLANTA DO TAMPO 1:10

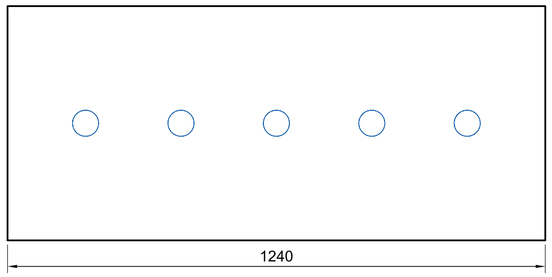

ESPECIFICAÇÃO

Balcão em MDF 18 mm laminado branco, 1200 x 950 x 500 mm, tampo 1240 x 540 mm.
Frente em PS 2 mm impresso com a arte do KV, fixada com fita VHB.
Testeira 1200 x 400 mm em PS 2 mm sobre 2 hastes em tubo Ø25 mm, altura total 2100 mm.
Tampo com 5 borrifadores (um por fragrância) e porta-fitas olfativas.
Porta de serviço no verso para estoque de fitas e frascos.
Desmonta em 3 volumes (balcão, hastes, testeira) para transporte.
Lugar: área promocional ao lado da entrada do corredor de limpeza, sem bloquear a passagem.
Operação: 1 promotor em turnos de 6 h, fim de semana.

PERSPECTIVA ILUSTRATIVA (sem escala)



75LAB projetos de PDV · 75lab.com.br	PROJETO: Escolha o perfume da sua casa · PDV		
CLIENTE: Bombril · Limpol Perfumes	MATERIAL: MDF 18 mm laminado; tubo Ø25; PS 2 mm		
CONTEÚDO DA FOLHA: Estação de aroma · vistas Conjunto pesado · ativação em loja			
ESCALA: 1:10	UNIDADE: mm	DATA: 20/10/2026	FOLHA: 02 / 05
REVISÃO: R00 · proposta	DESENHO: 75 LAB	FORMATO: A2 · 1º diedro	ARQUIVO: P2_estacao-de-aroma.dxf

Medidas em mm pela linha de molde externa. Não medir no desenho; em caso de dúvida, valem as cotas.